
Rendered sketch


New home build · Draft F · Oct 25, 2026

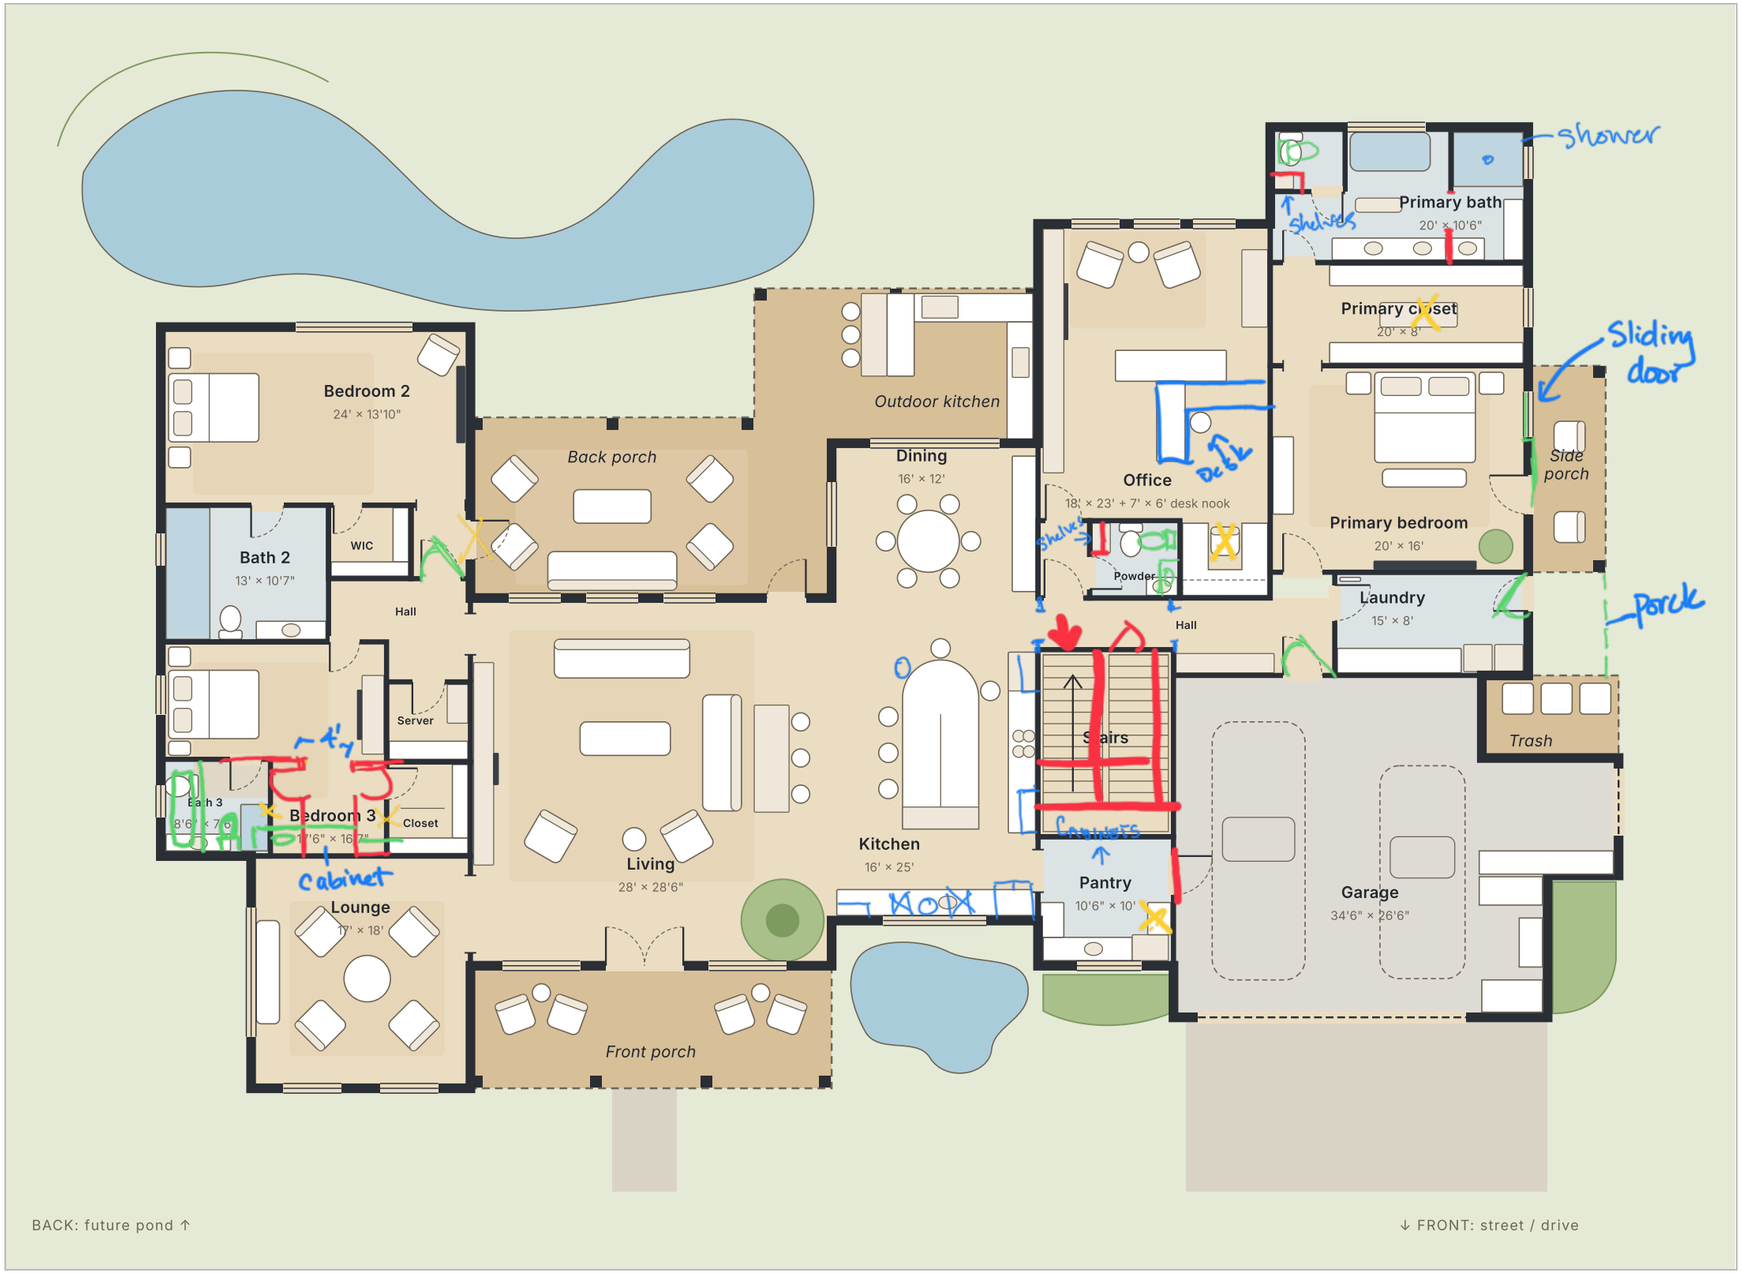

Markup notes: circle, arrow and write anywhere. Back (pond) is at the top.


Blueprint, main floor (1 square = 2 ft)

New home build · Draft F · Oct 25, 2026

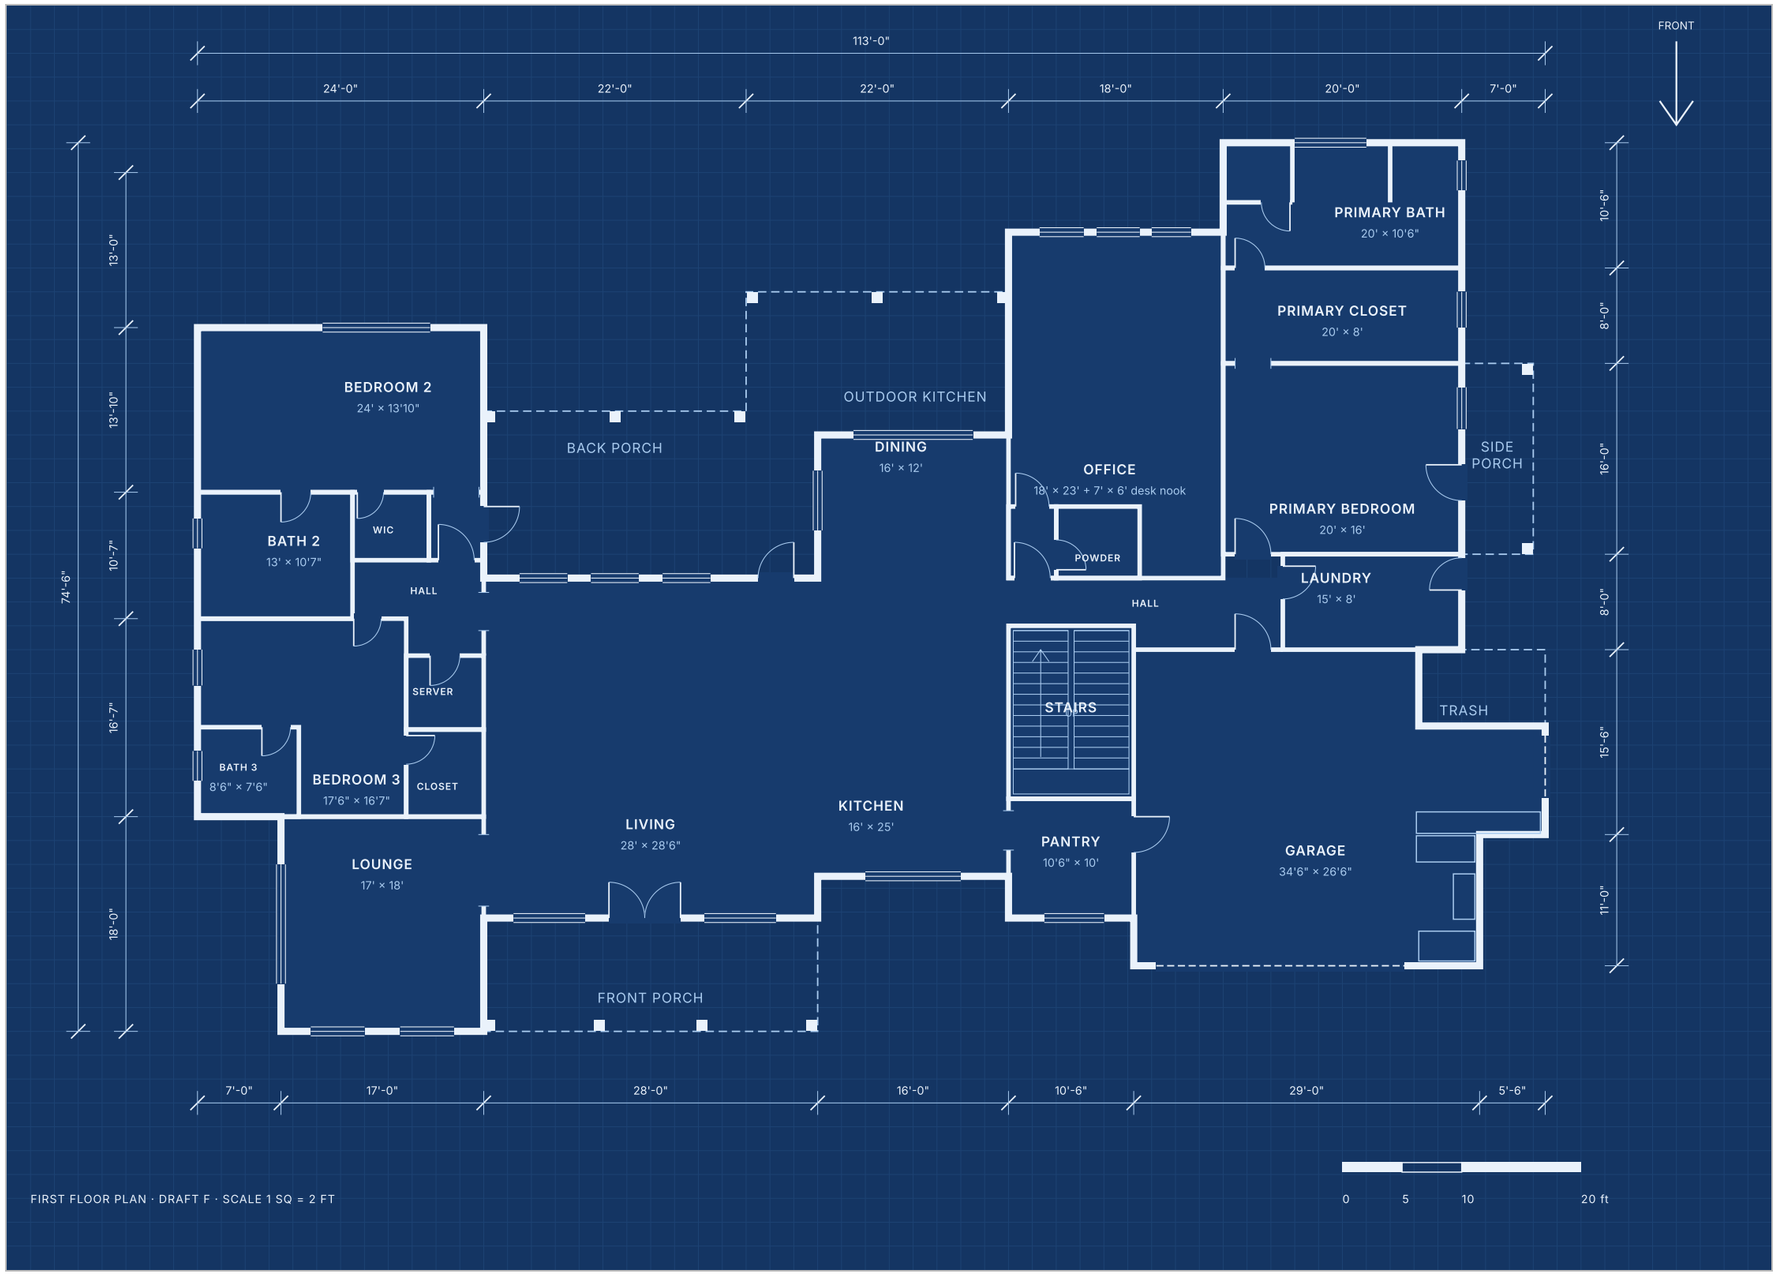


Markup notes: circle, arrow and write anywhere. Back (pond) is at the top.


Garage and upstairs options

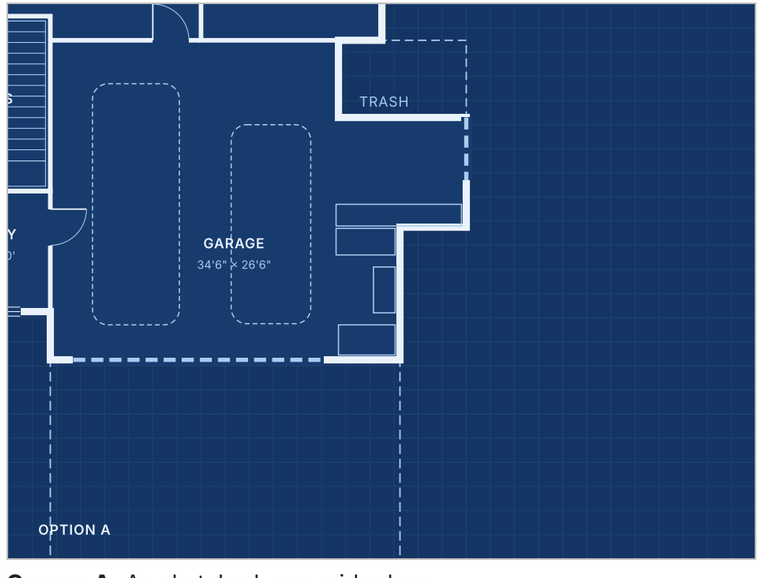


Garage A. As sketched, one wide door

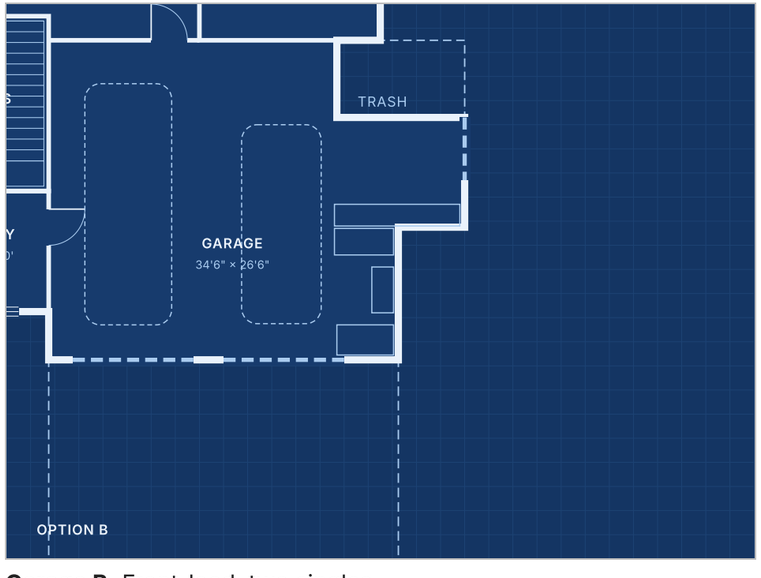


Garage B. Front-load, two singles

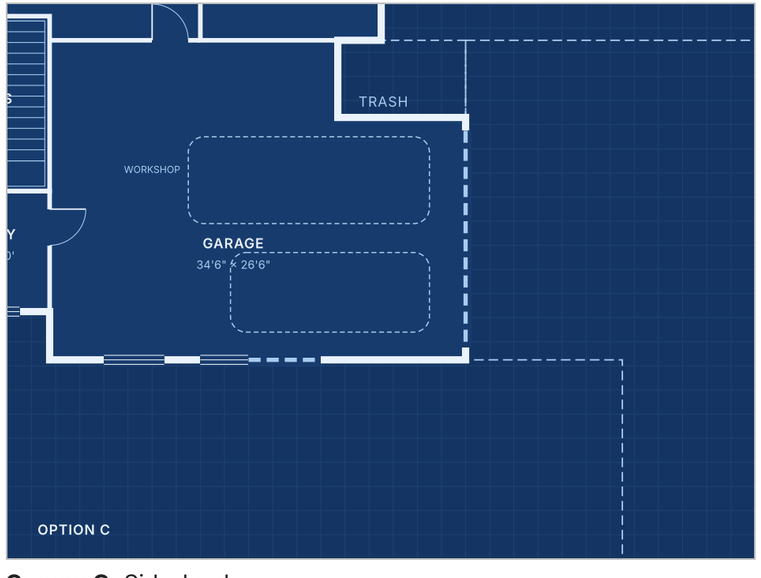

Garage C. Side-load

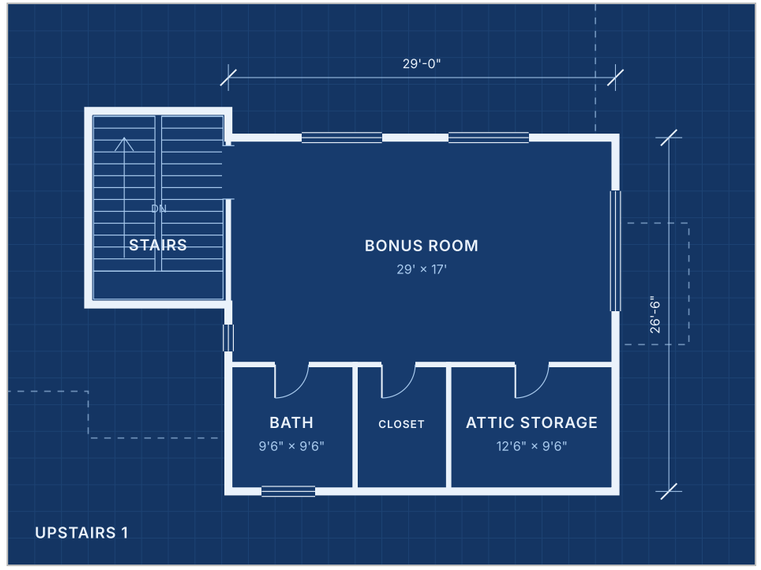

Upstairs 1. One bonus room

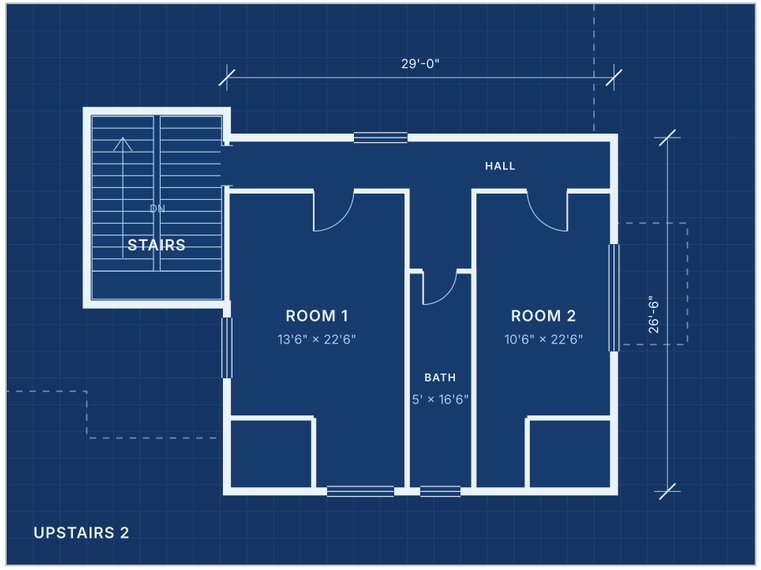

Upstairs 2. Two rooms

Markup notes